
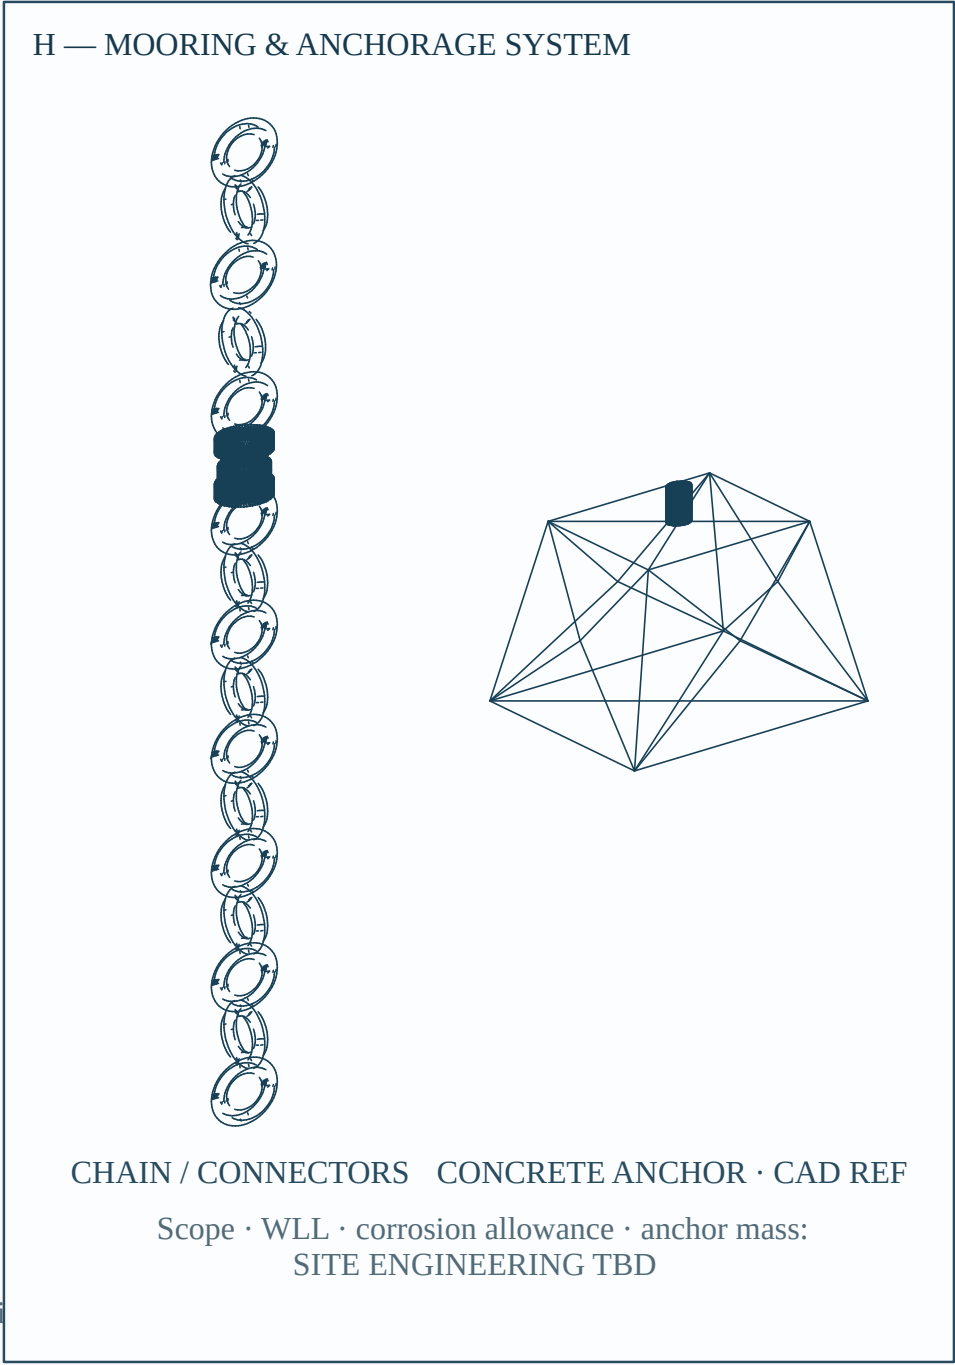
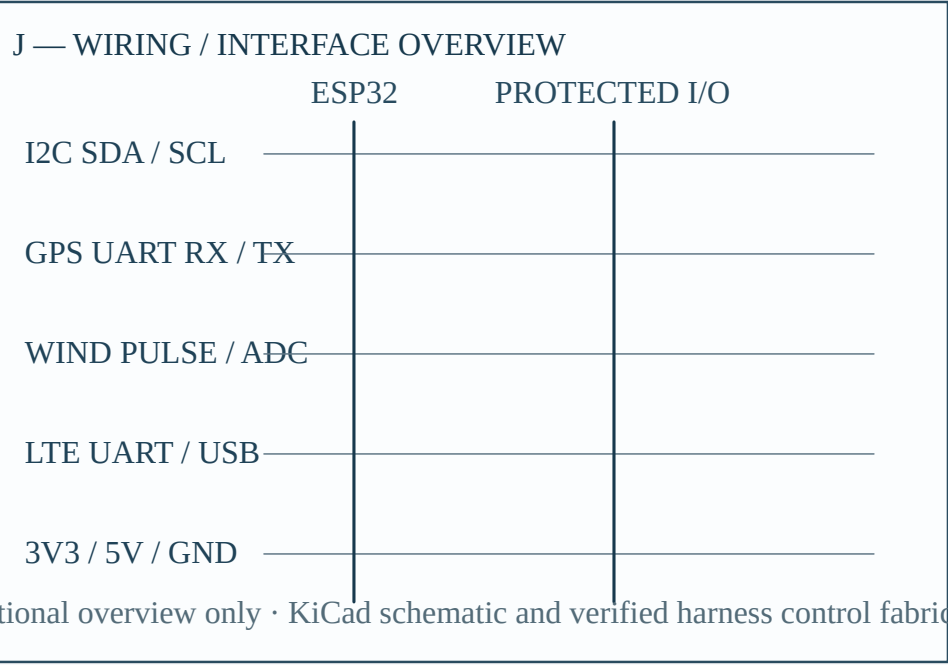
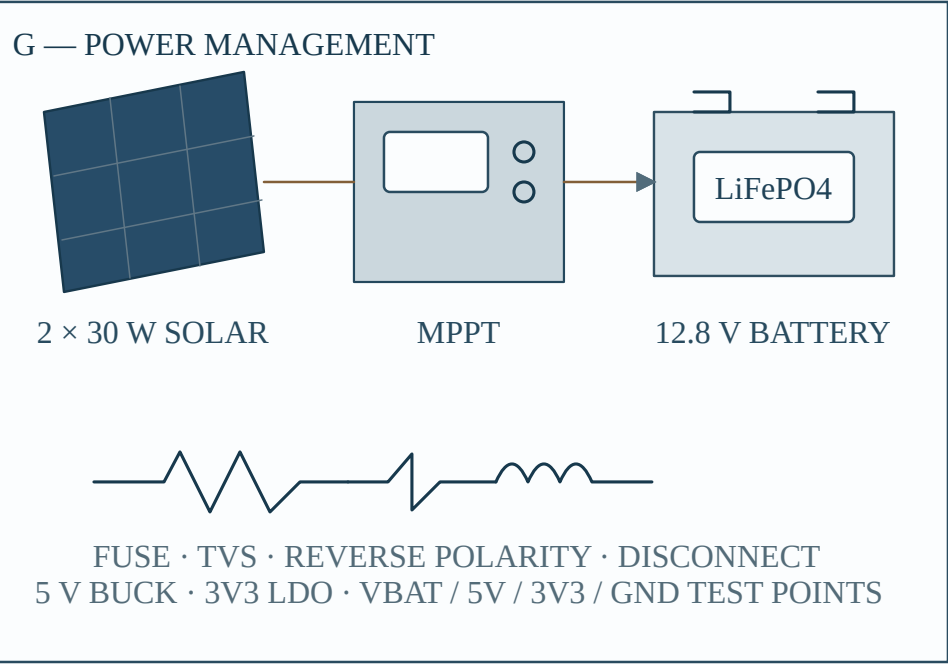
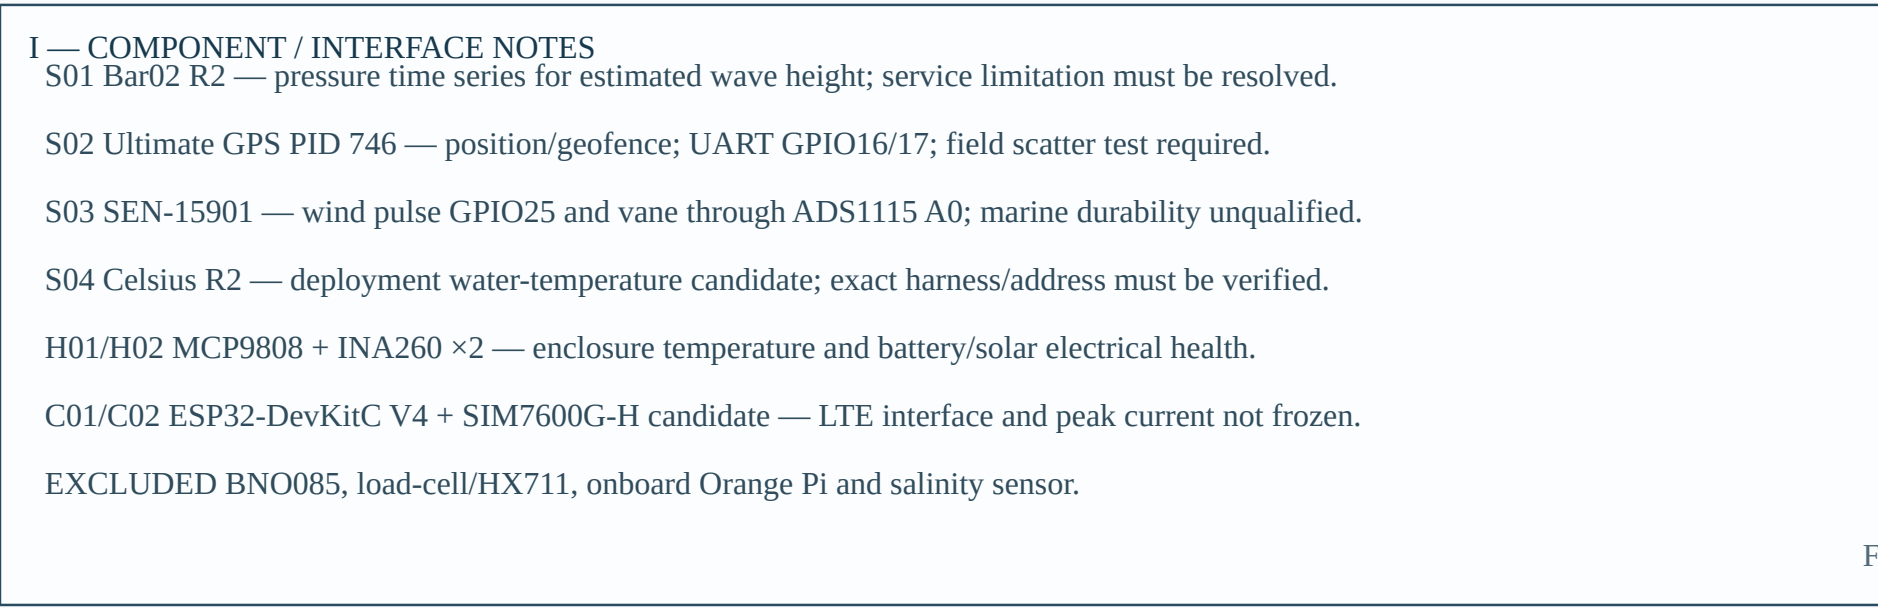
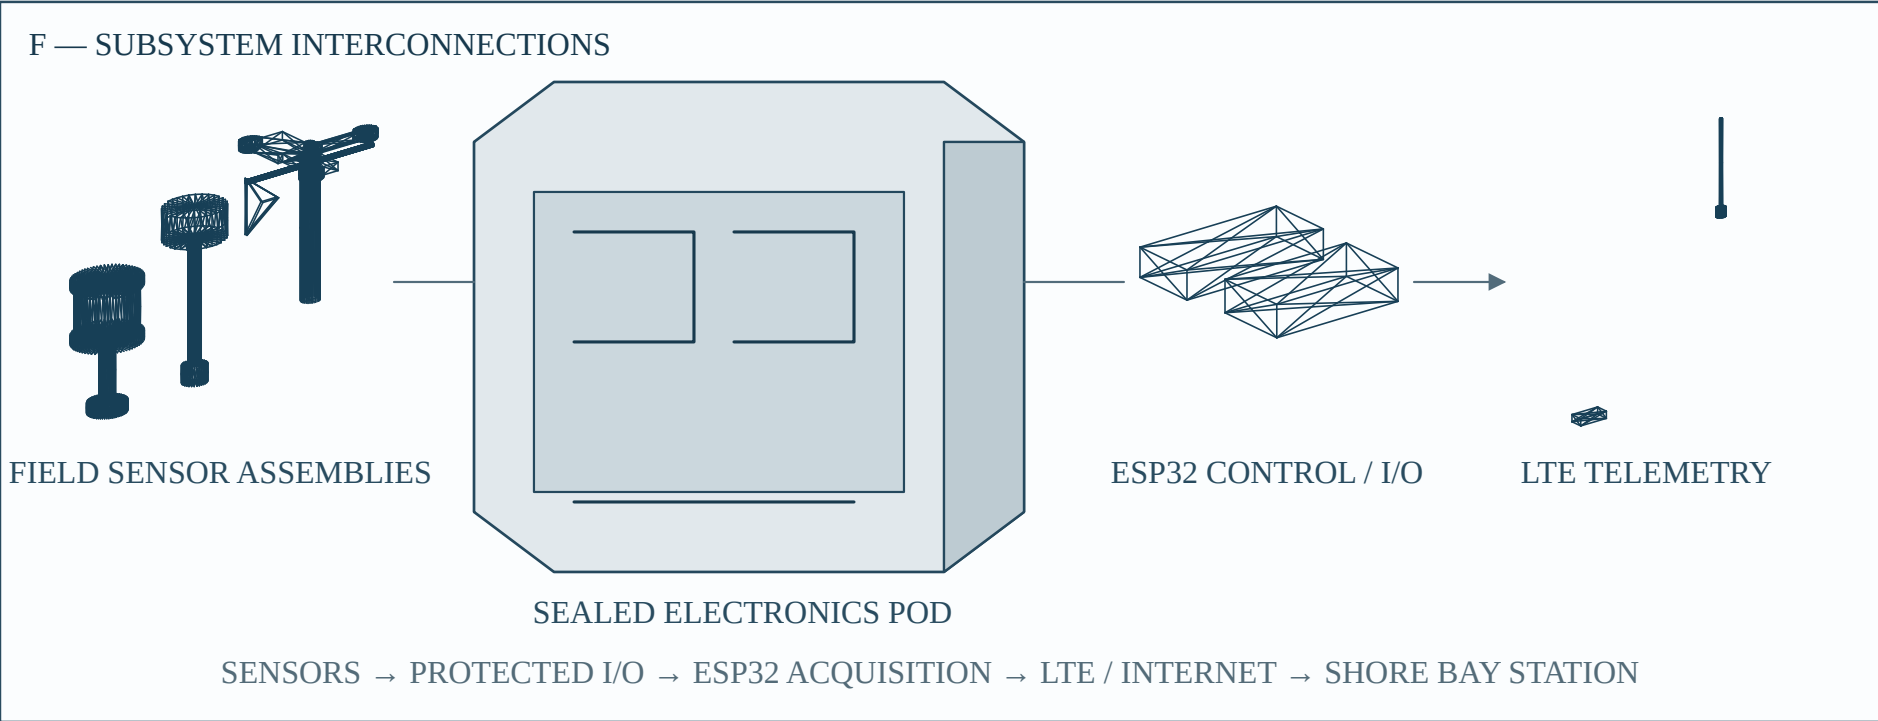
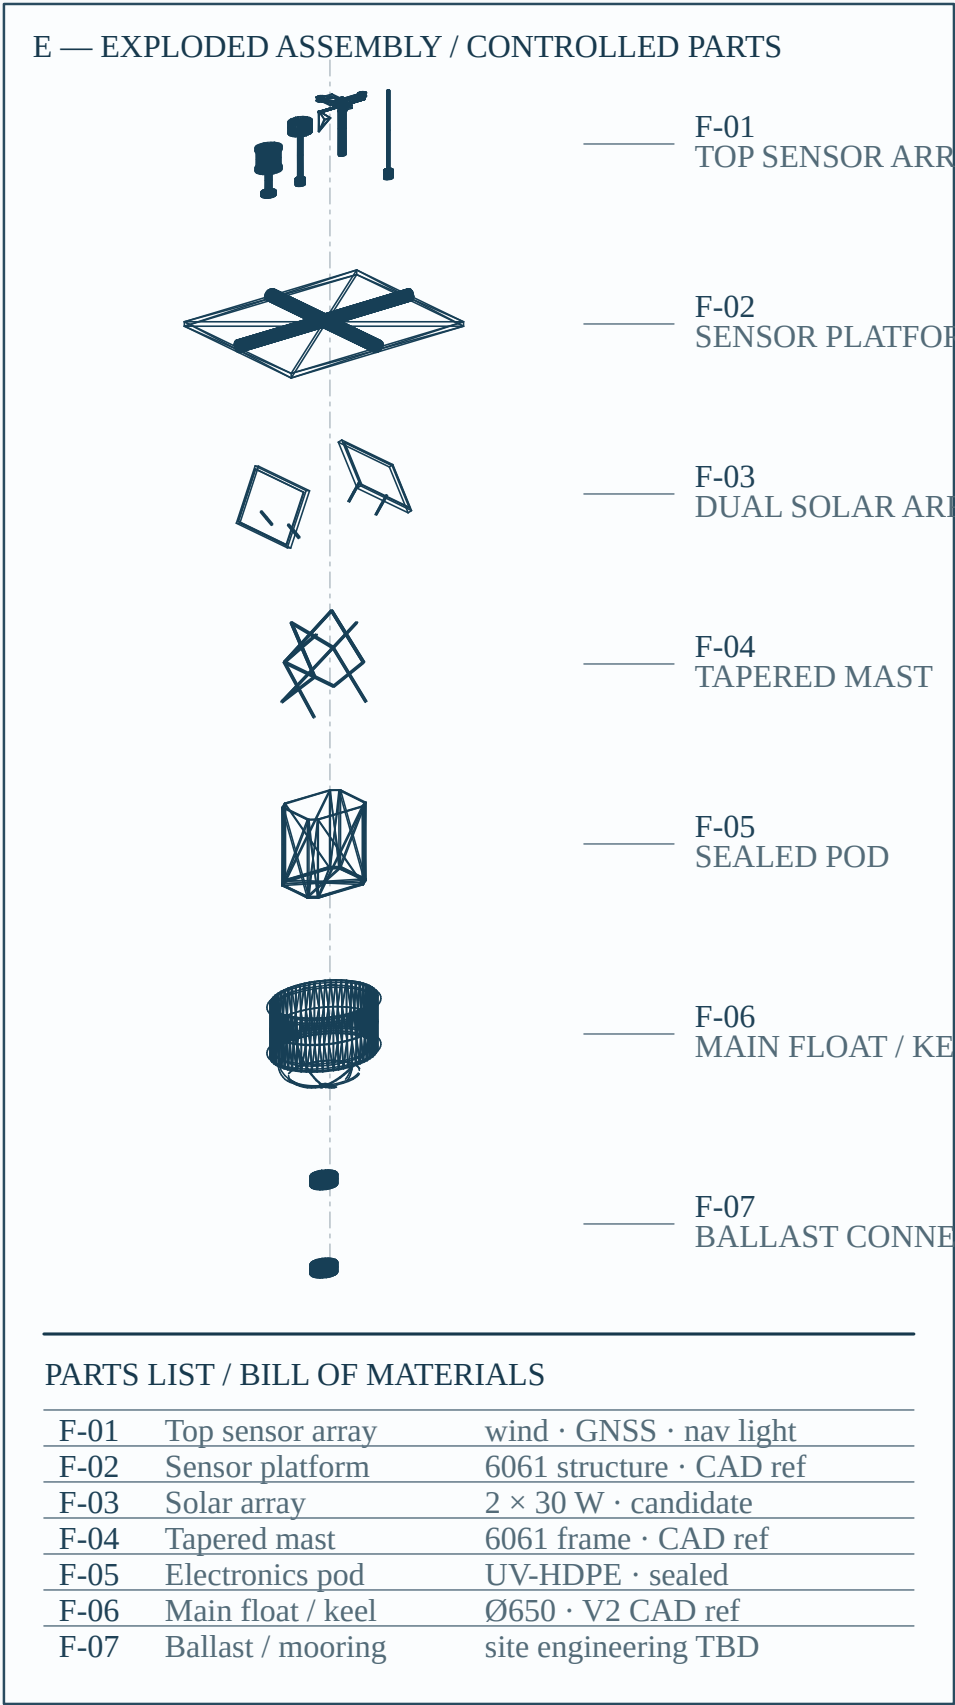
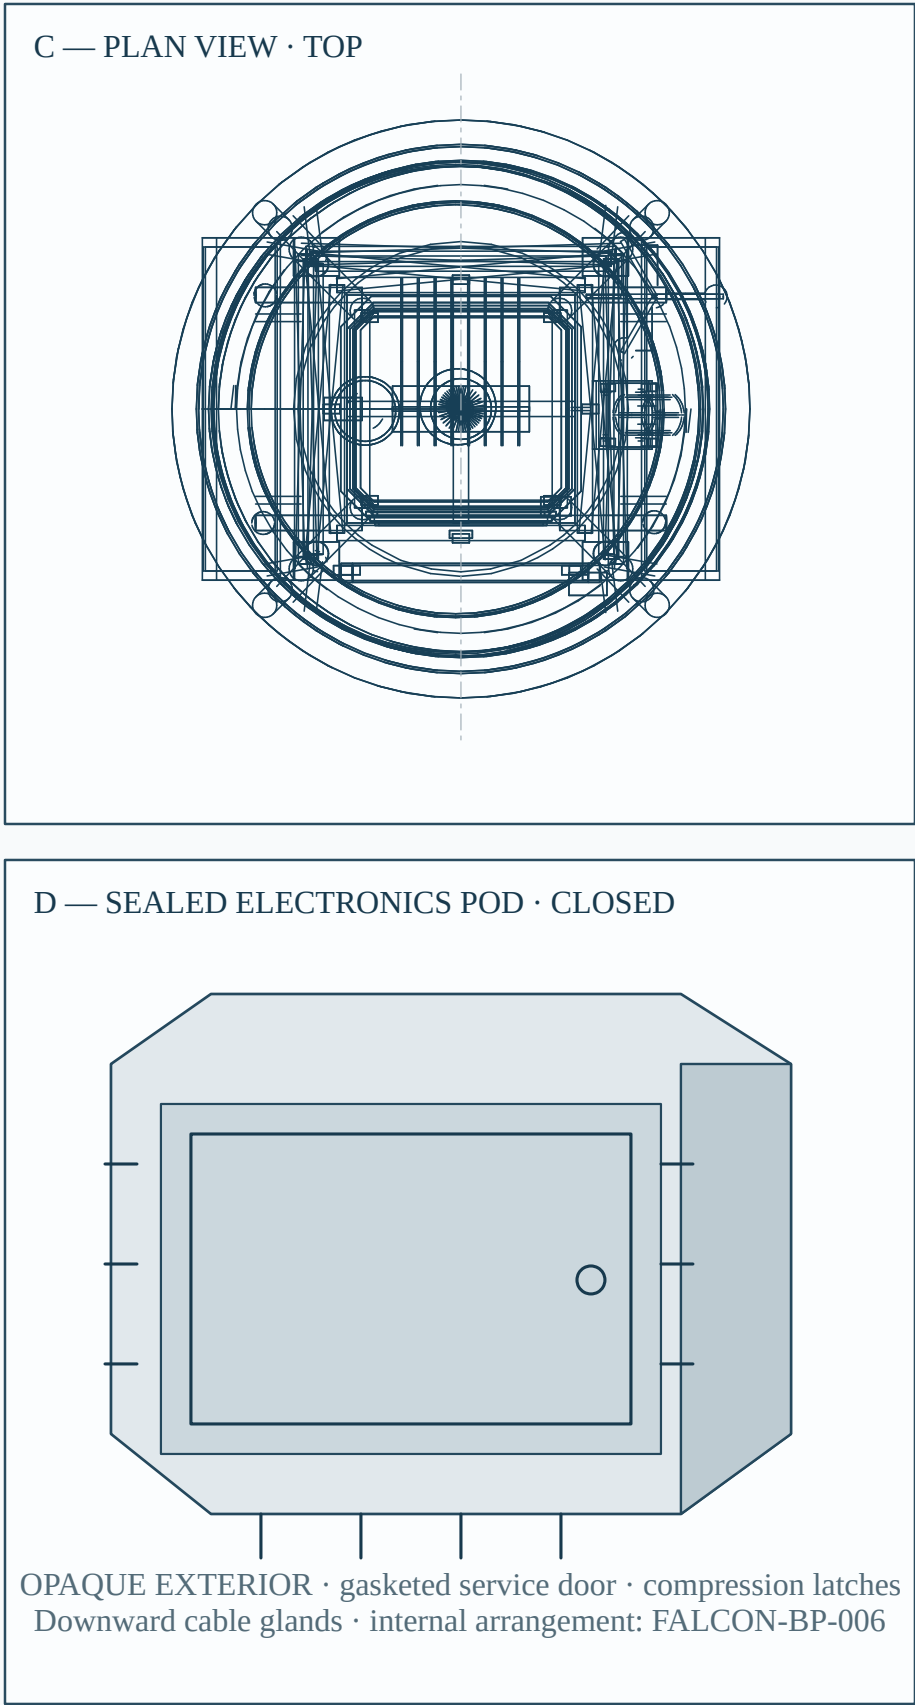
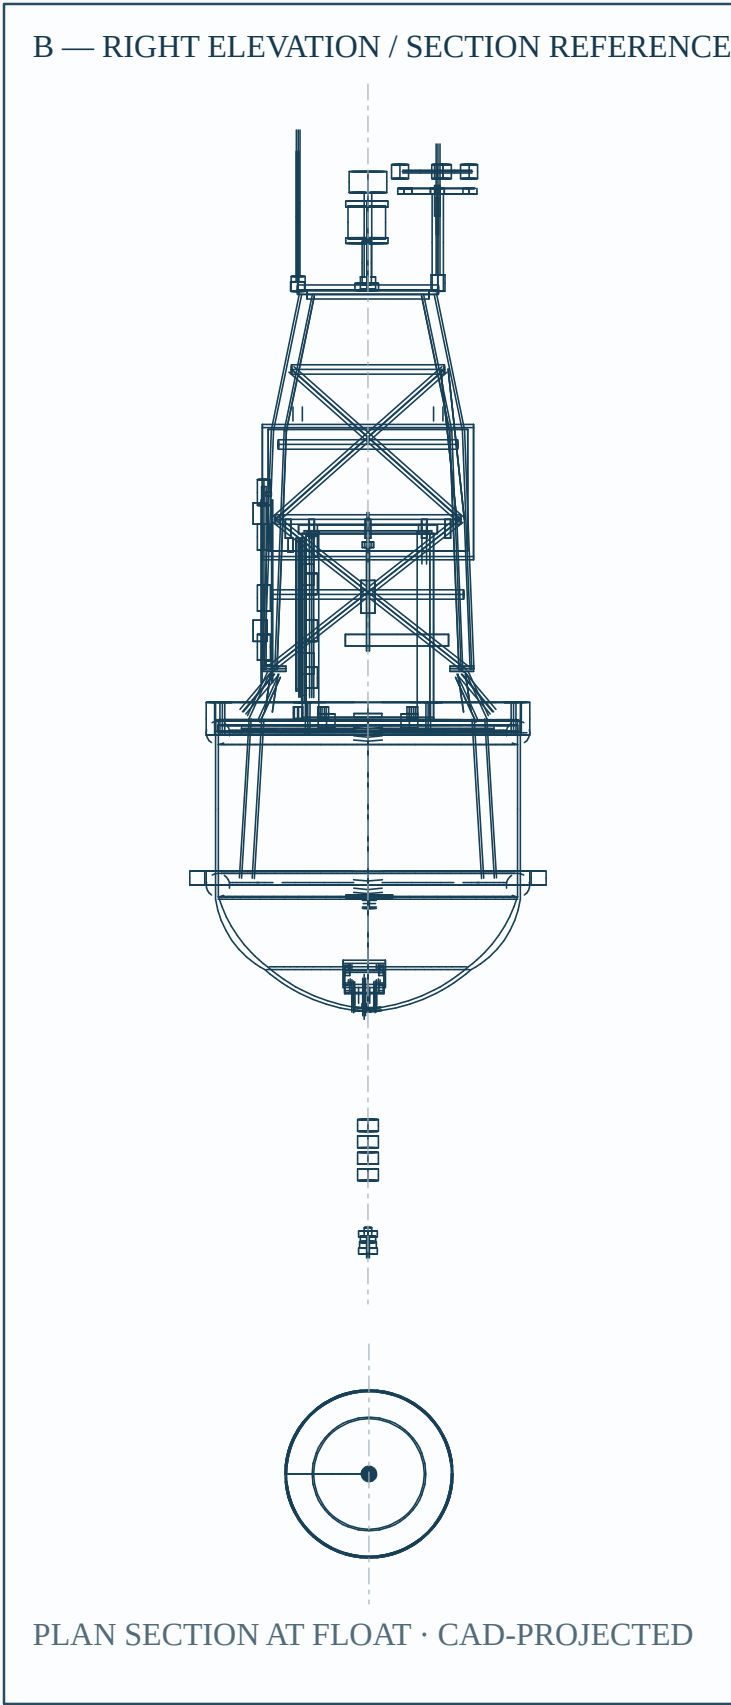


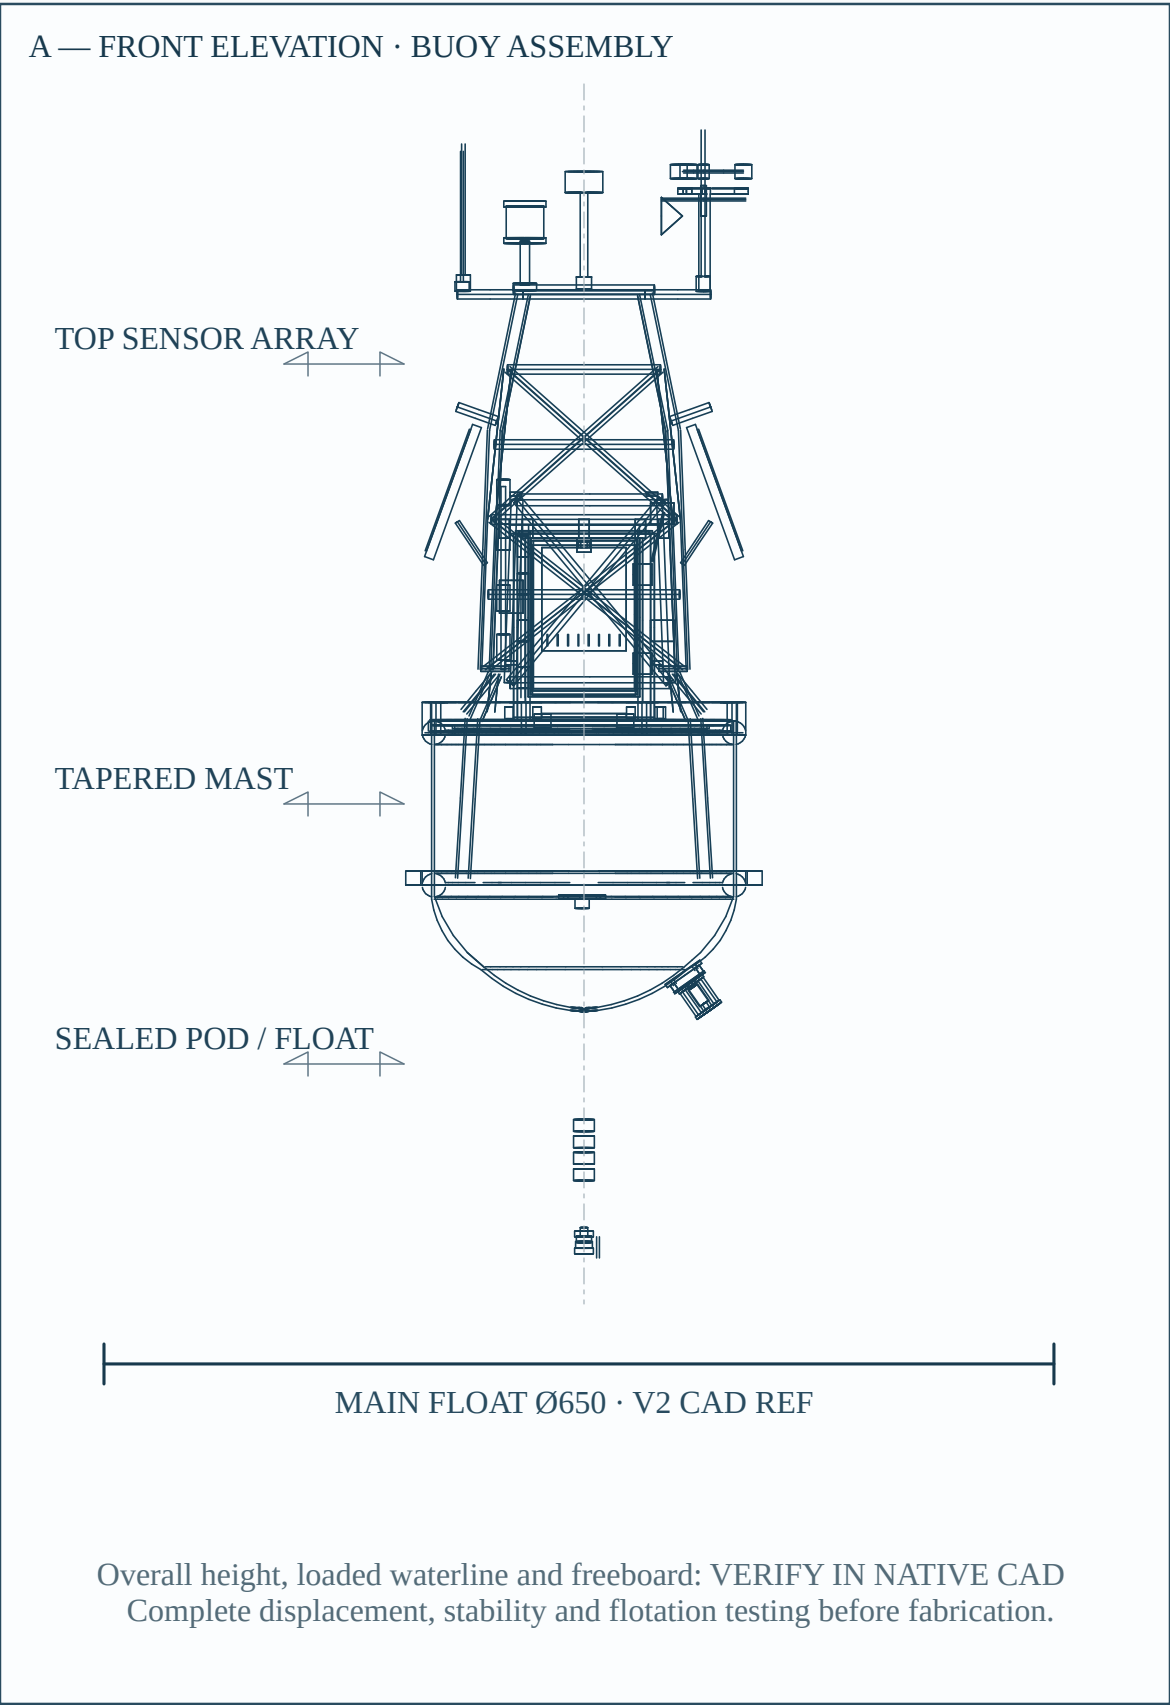

GENERAL NOTES	
1.	CAD linework is projected from PROJECT-FALCON-V2.glb; do not scale this sheet.
2.	Project FALCON estimates wave height from submerged pressure time series at the shore Bay Station.
3.	Orange Pi / Bay Station computer remains ashore; no single-board computer is installed on the buoy.
4.	Verify purchased components, pin 1, voltages, connector orientation, sealing, loads and calibration.
5.	Complete flotation, stability, structure, thermal, ingress, corrosion, power and mooring reviews before build.
REFERENCE / NOT FOR FABRICATION	

DRAWING CONTROL		DRAWING TITLE ASSEMBLY & SUBSYSTEMS	
PROJECT FALCON-01			
DRAWING NO. FALCON-BP-000		REVISION	P2
SCALE NTS		DATE	2026-09-02
SOURCE V2 GLB + CONTROLLED DOCS		STATUS	REFERENCE / NOT FOR FABRICATION