
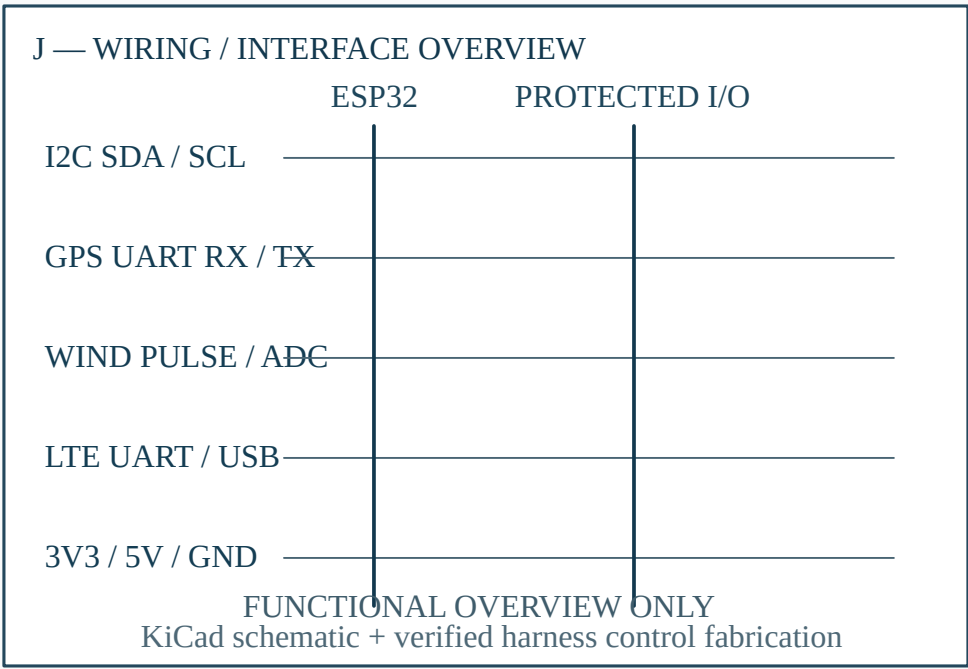
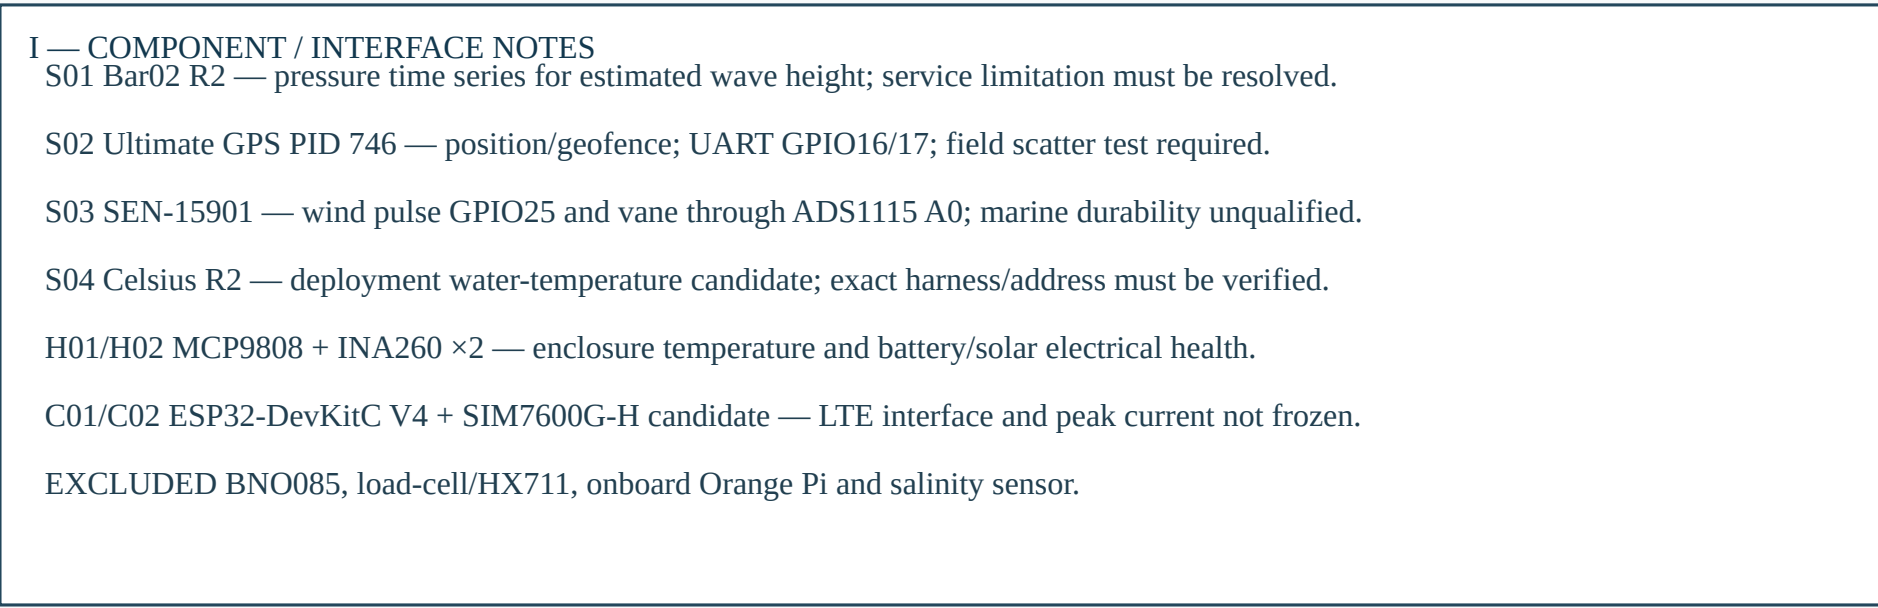
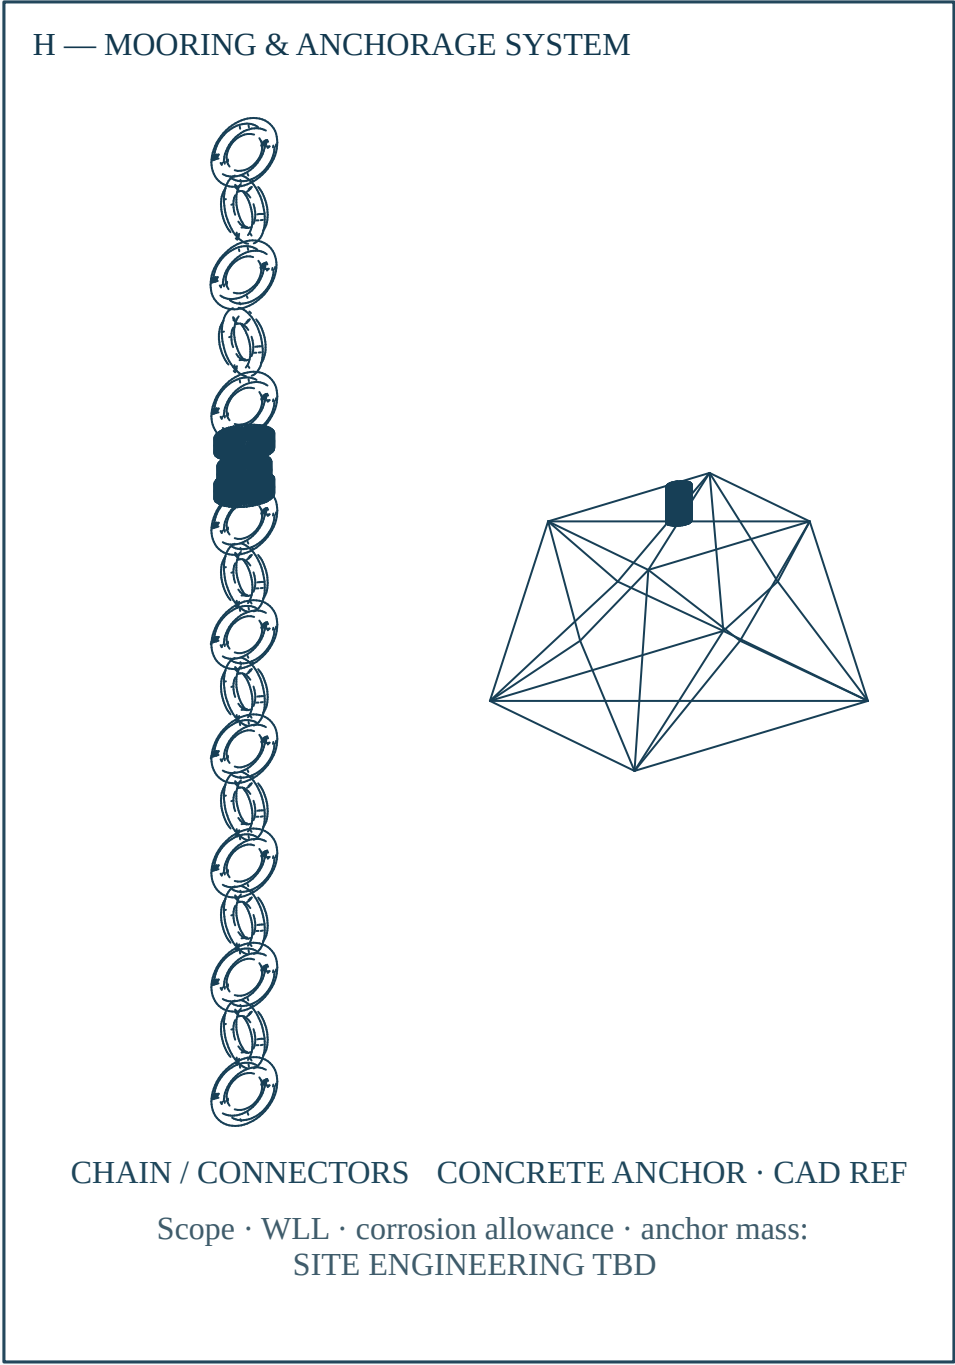
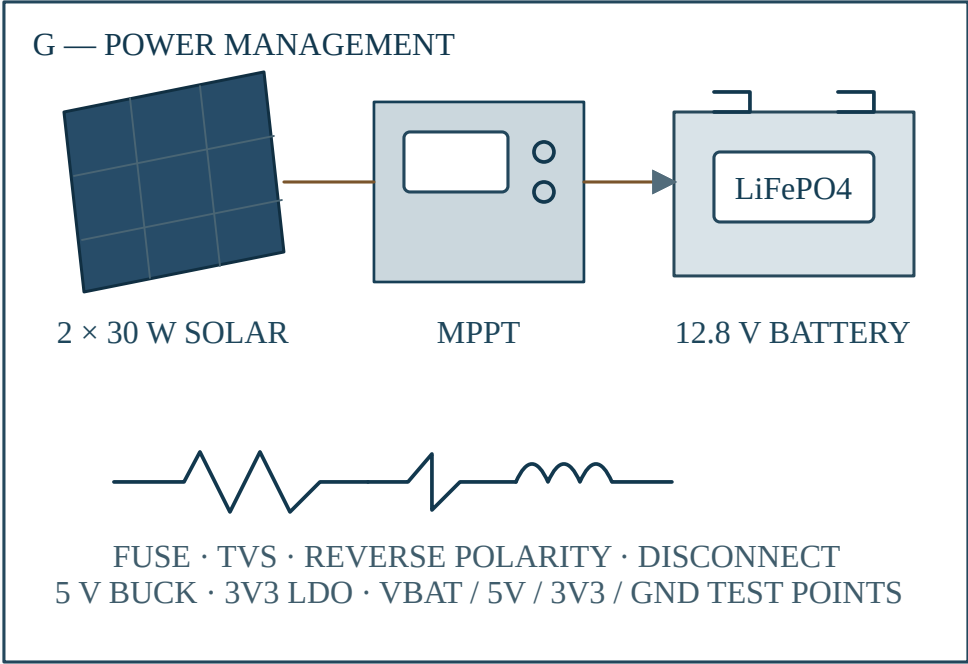
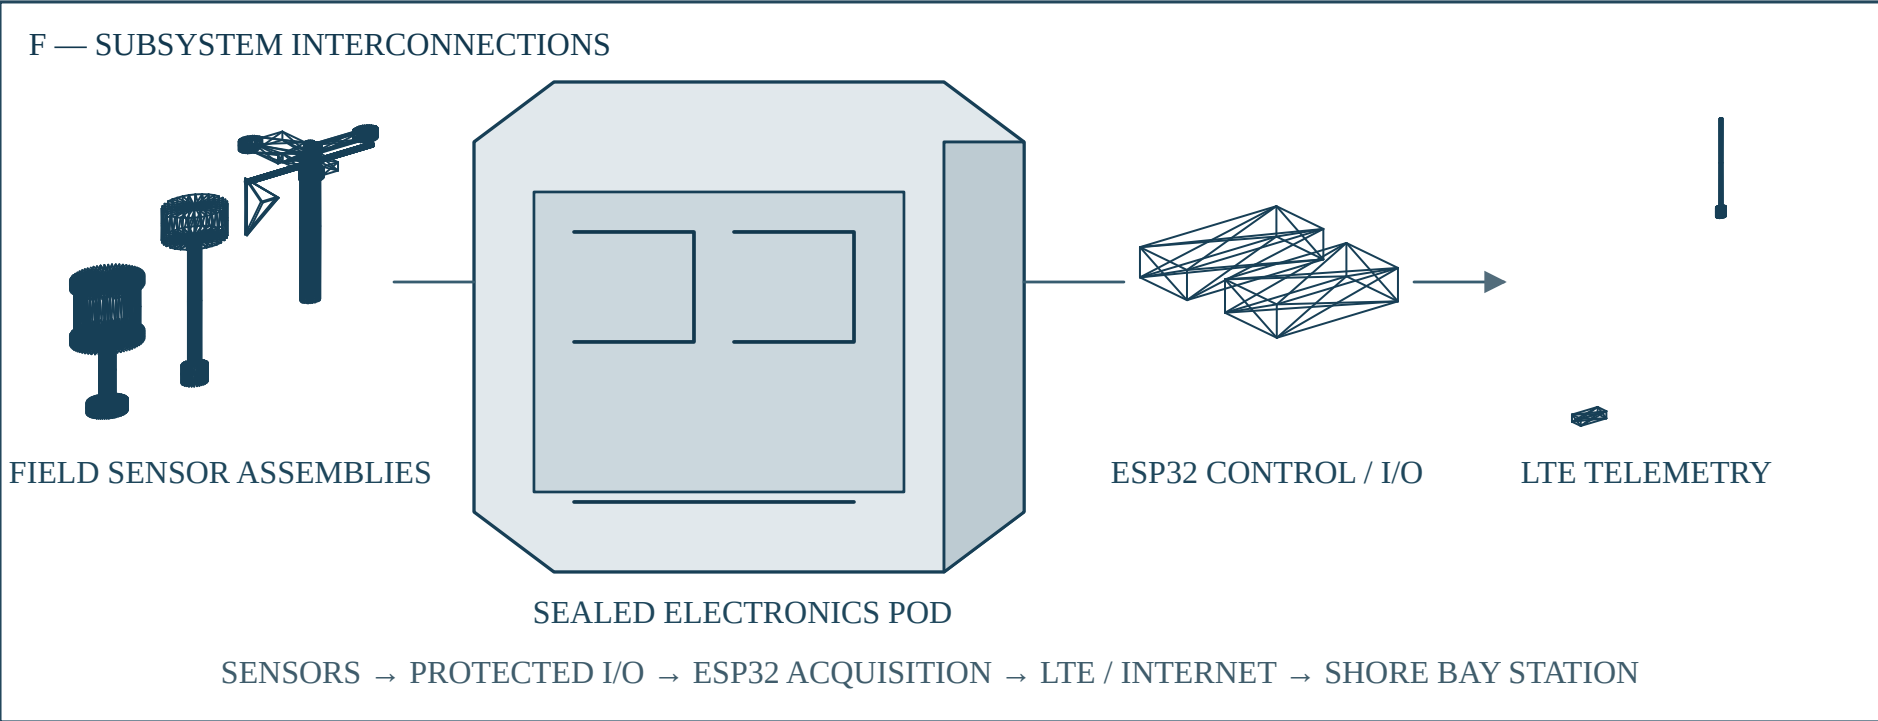
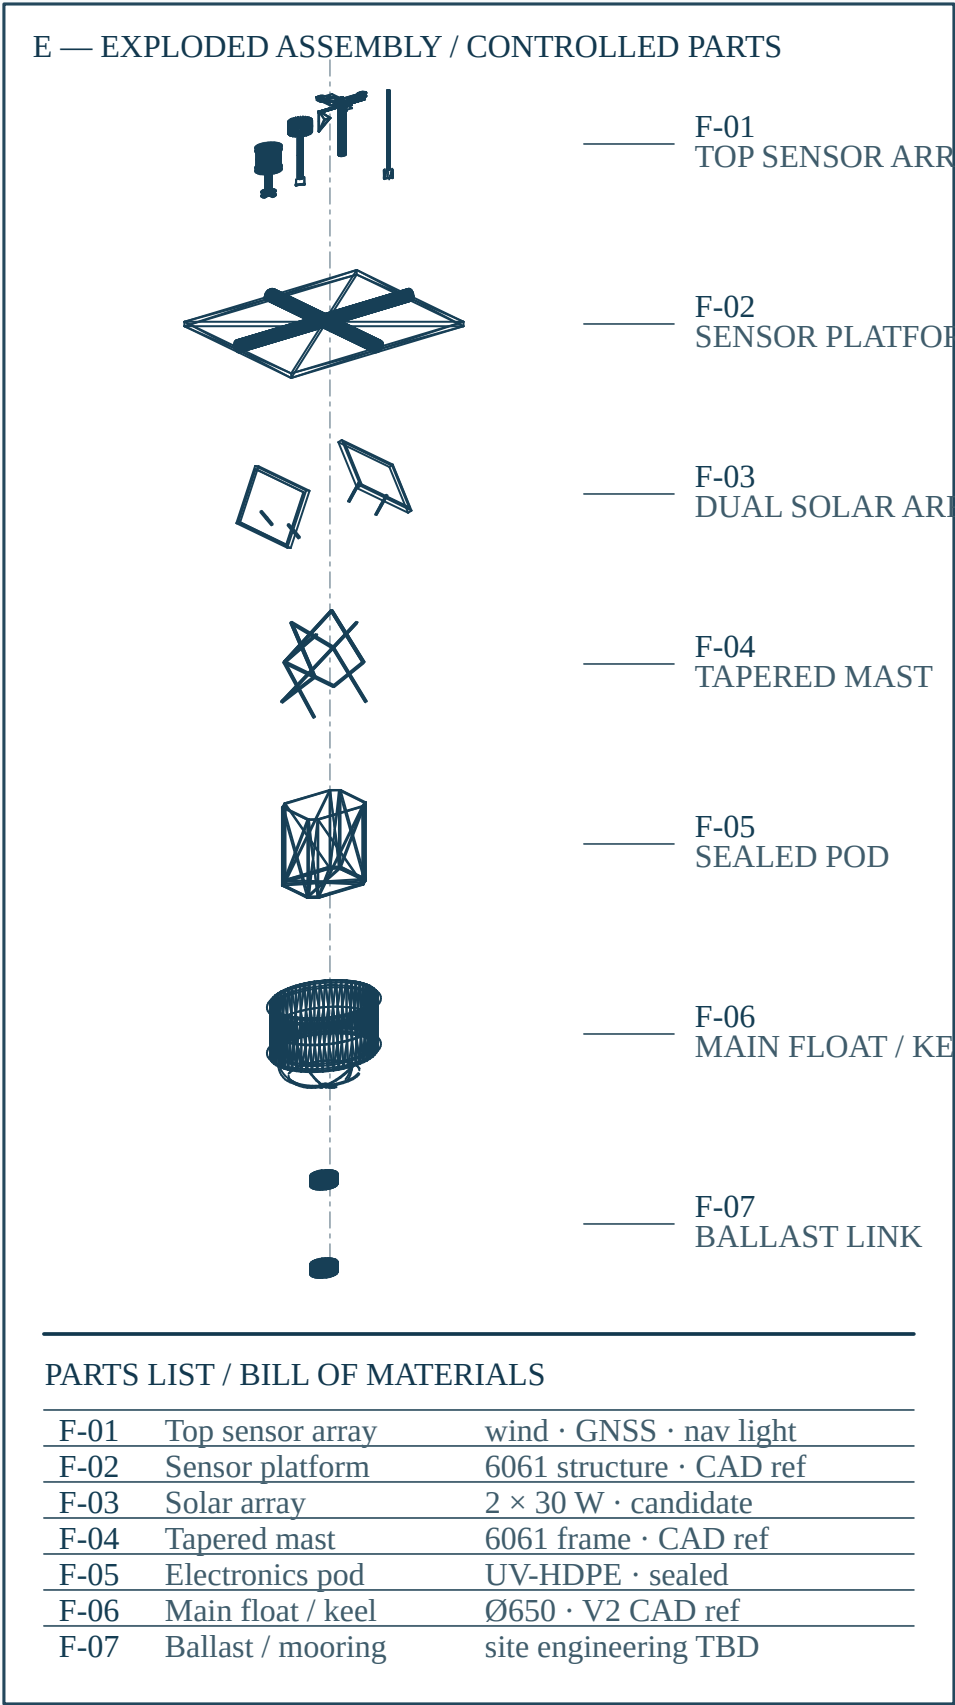
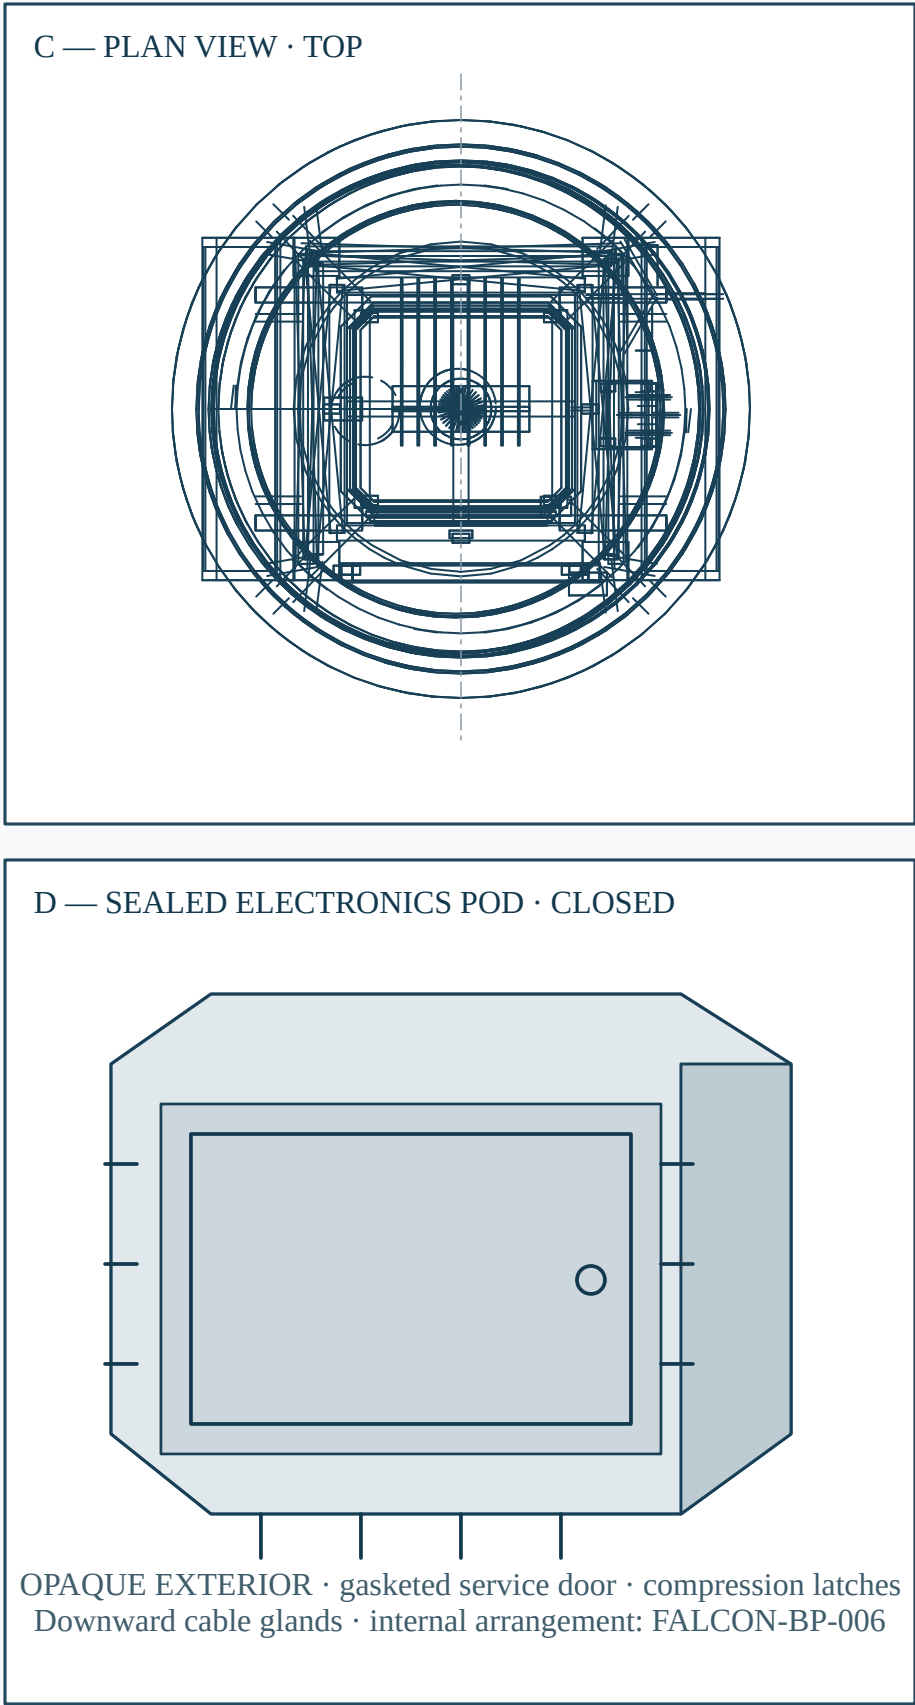
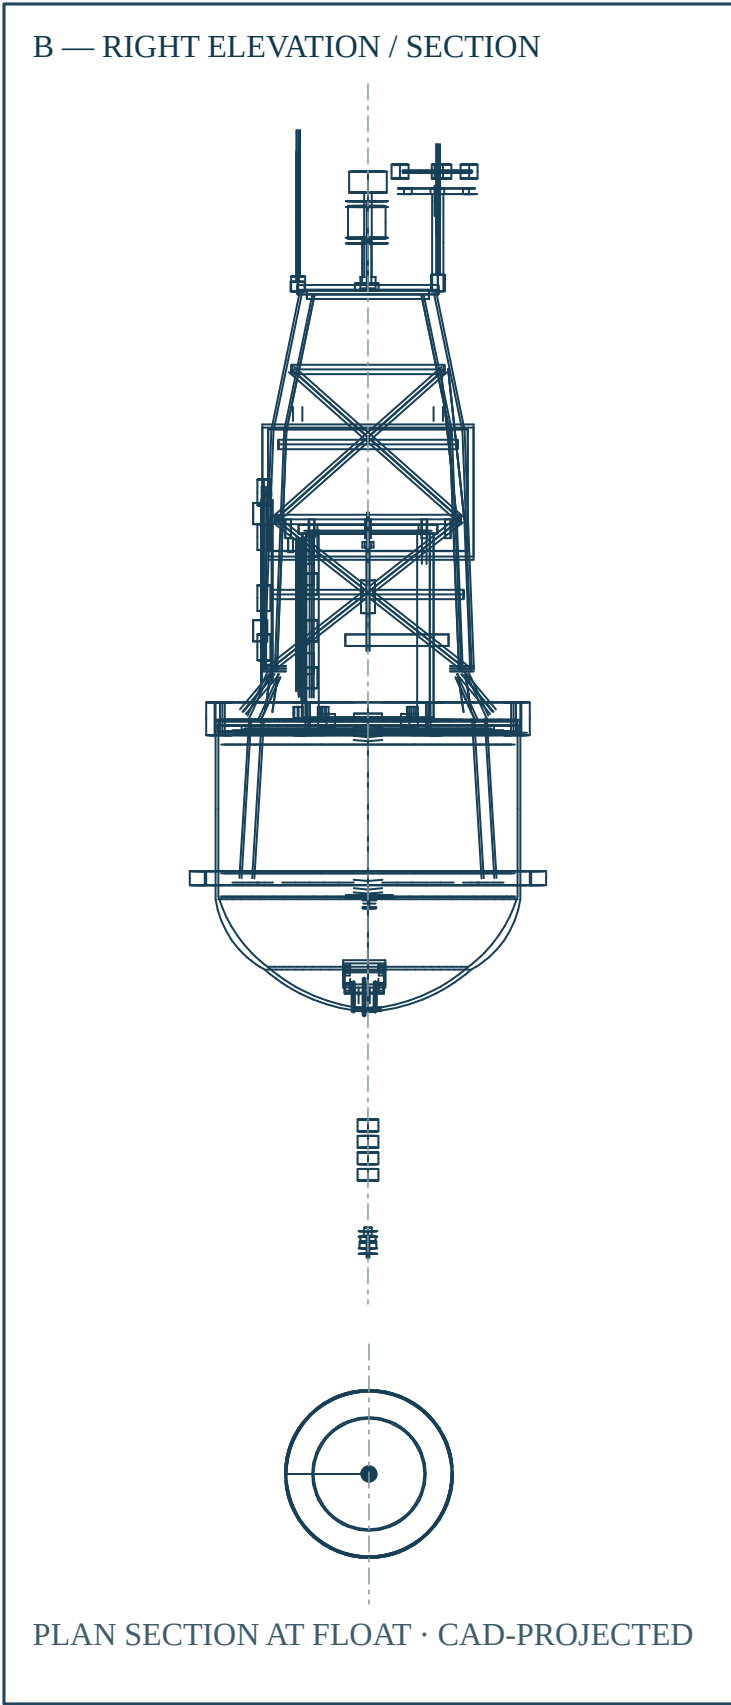


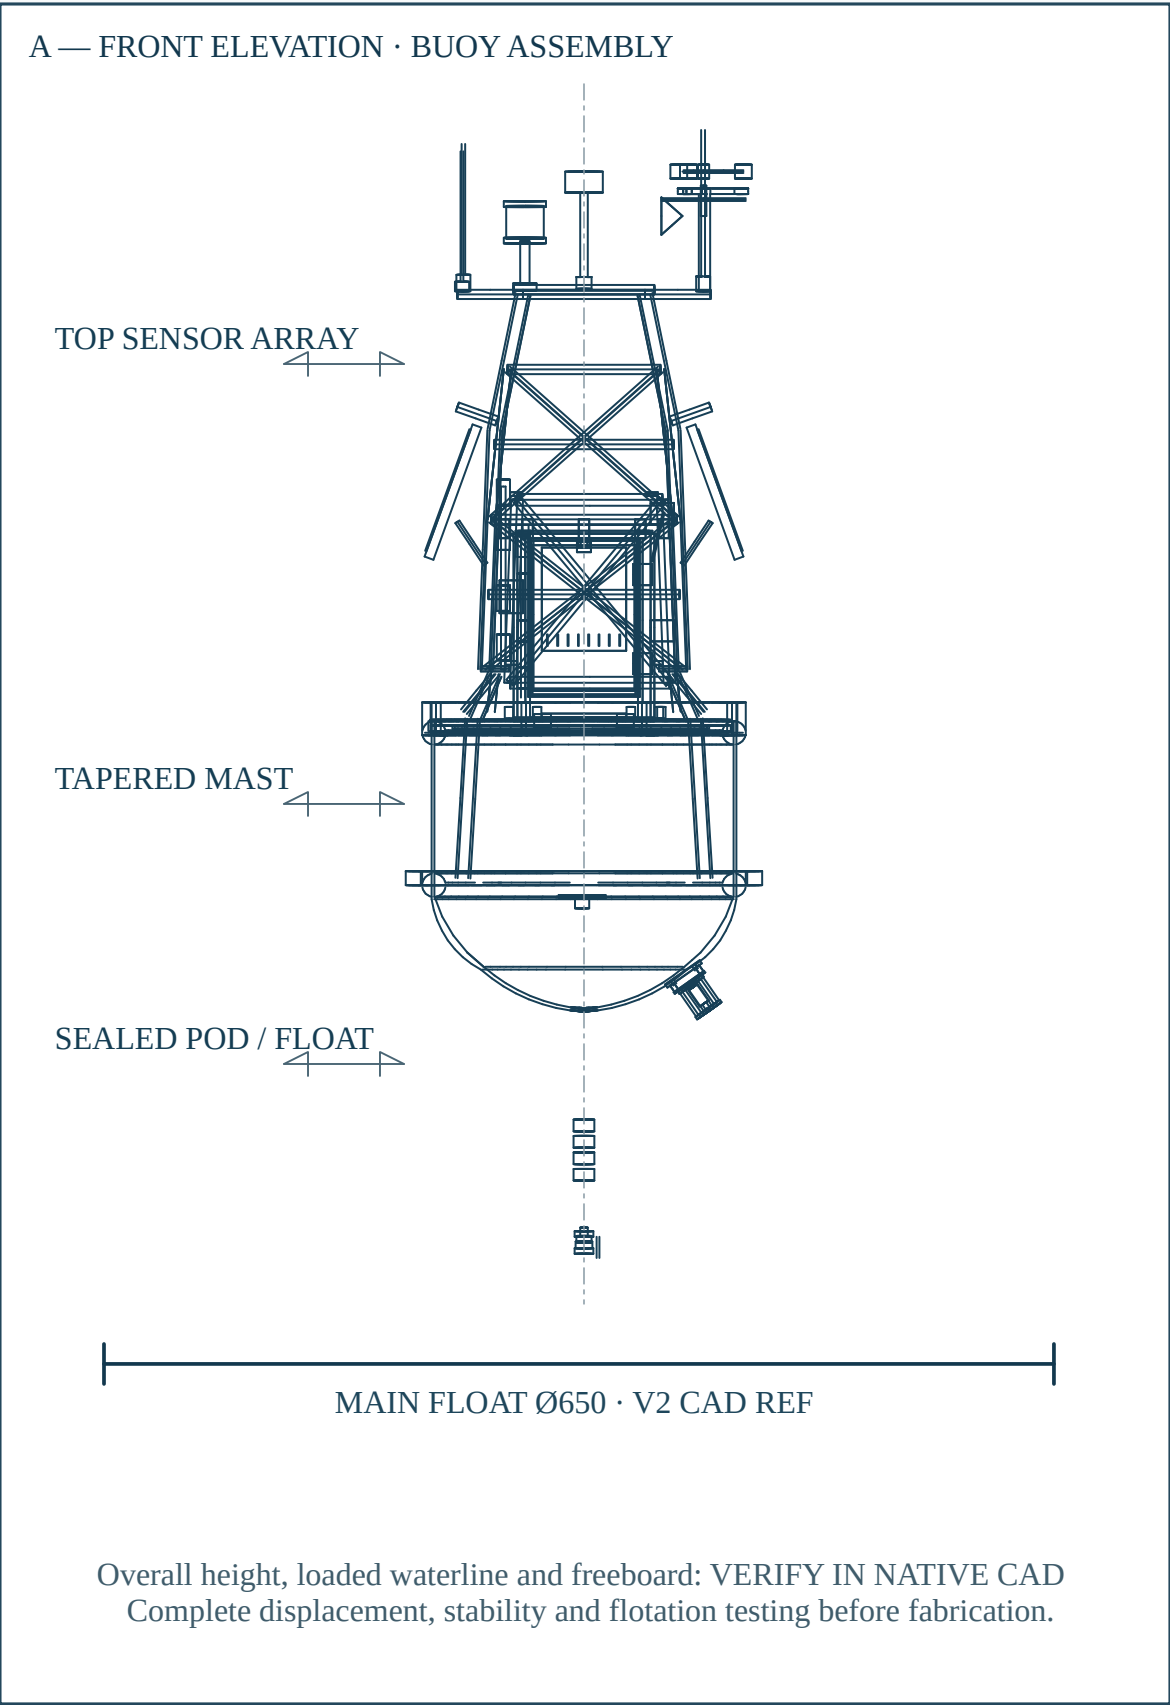

GENERAL NOTES	
1. CAD linework is projected from PROJECT-FALCON-V2.glb; do not scale this sheet.	
2. Project FALCON estimates wave height from submerged pressure time series at the shore Bay Station.	
3. Orange Pi / Bay Station computer remains ashore; no single-board computer is installed on the buoy.	
4. Verify purchased components, pin 1, voltages, connector orientation, sealing, loads and calibration.	
5. Complete flotation, stability, structure, thermal, ingress, corrosion, power and mooring reviews before build.	
REFERENCE / NOT FOR FABRICATION	

DRAWING CONTROL	DRAWING TITLE
PROJECT FALCON-01	ASSEMBLY & SUBSYSTEMS
DRAWING NO. FALCON-BP-000	REVISION P3
SCALE NTS	DATE 2026-09-03
SOURCE V2 GLB + CONTROLLED DOCS	STATUS REFERENCE / NOT FOR FABRICATION